


ACTUALIZACIÓN: 10/02/2021 8:18:11

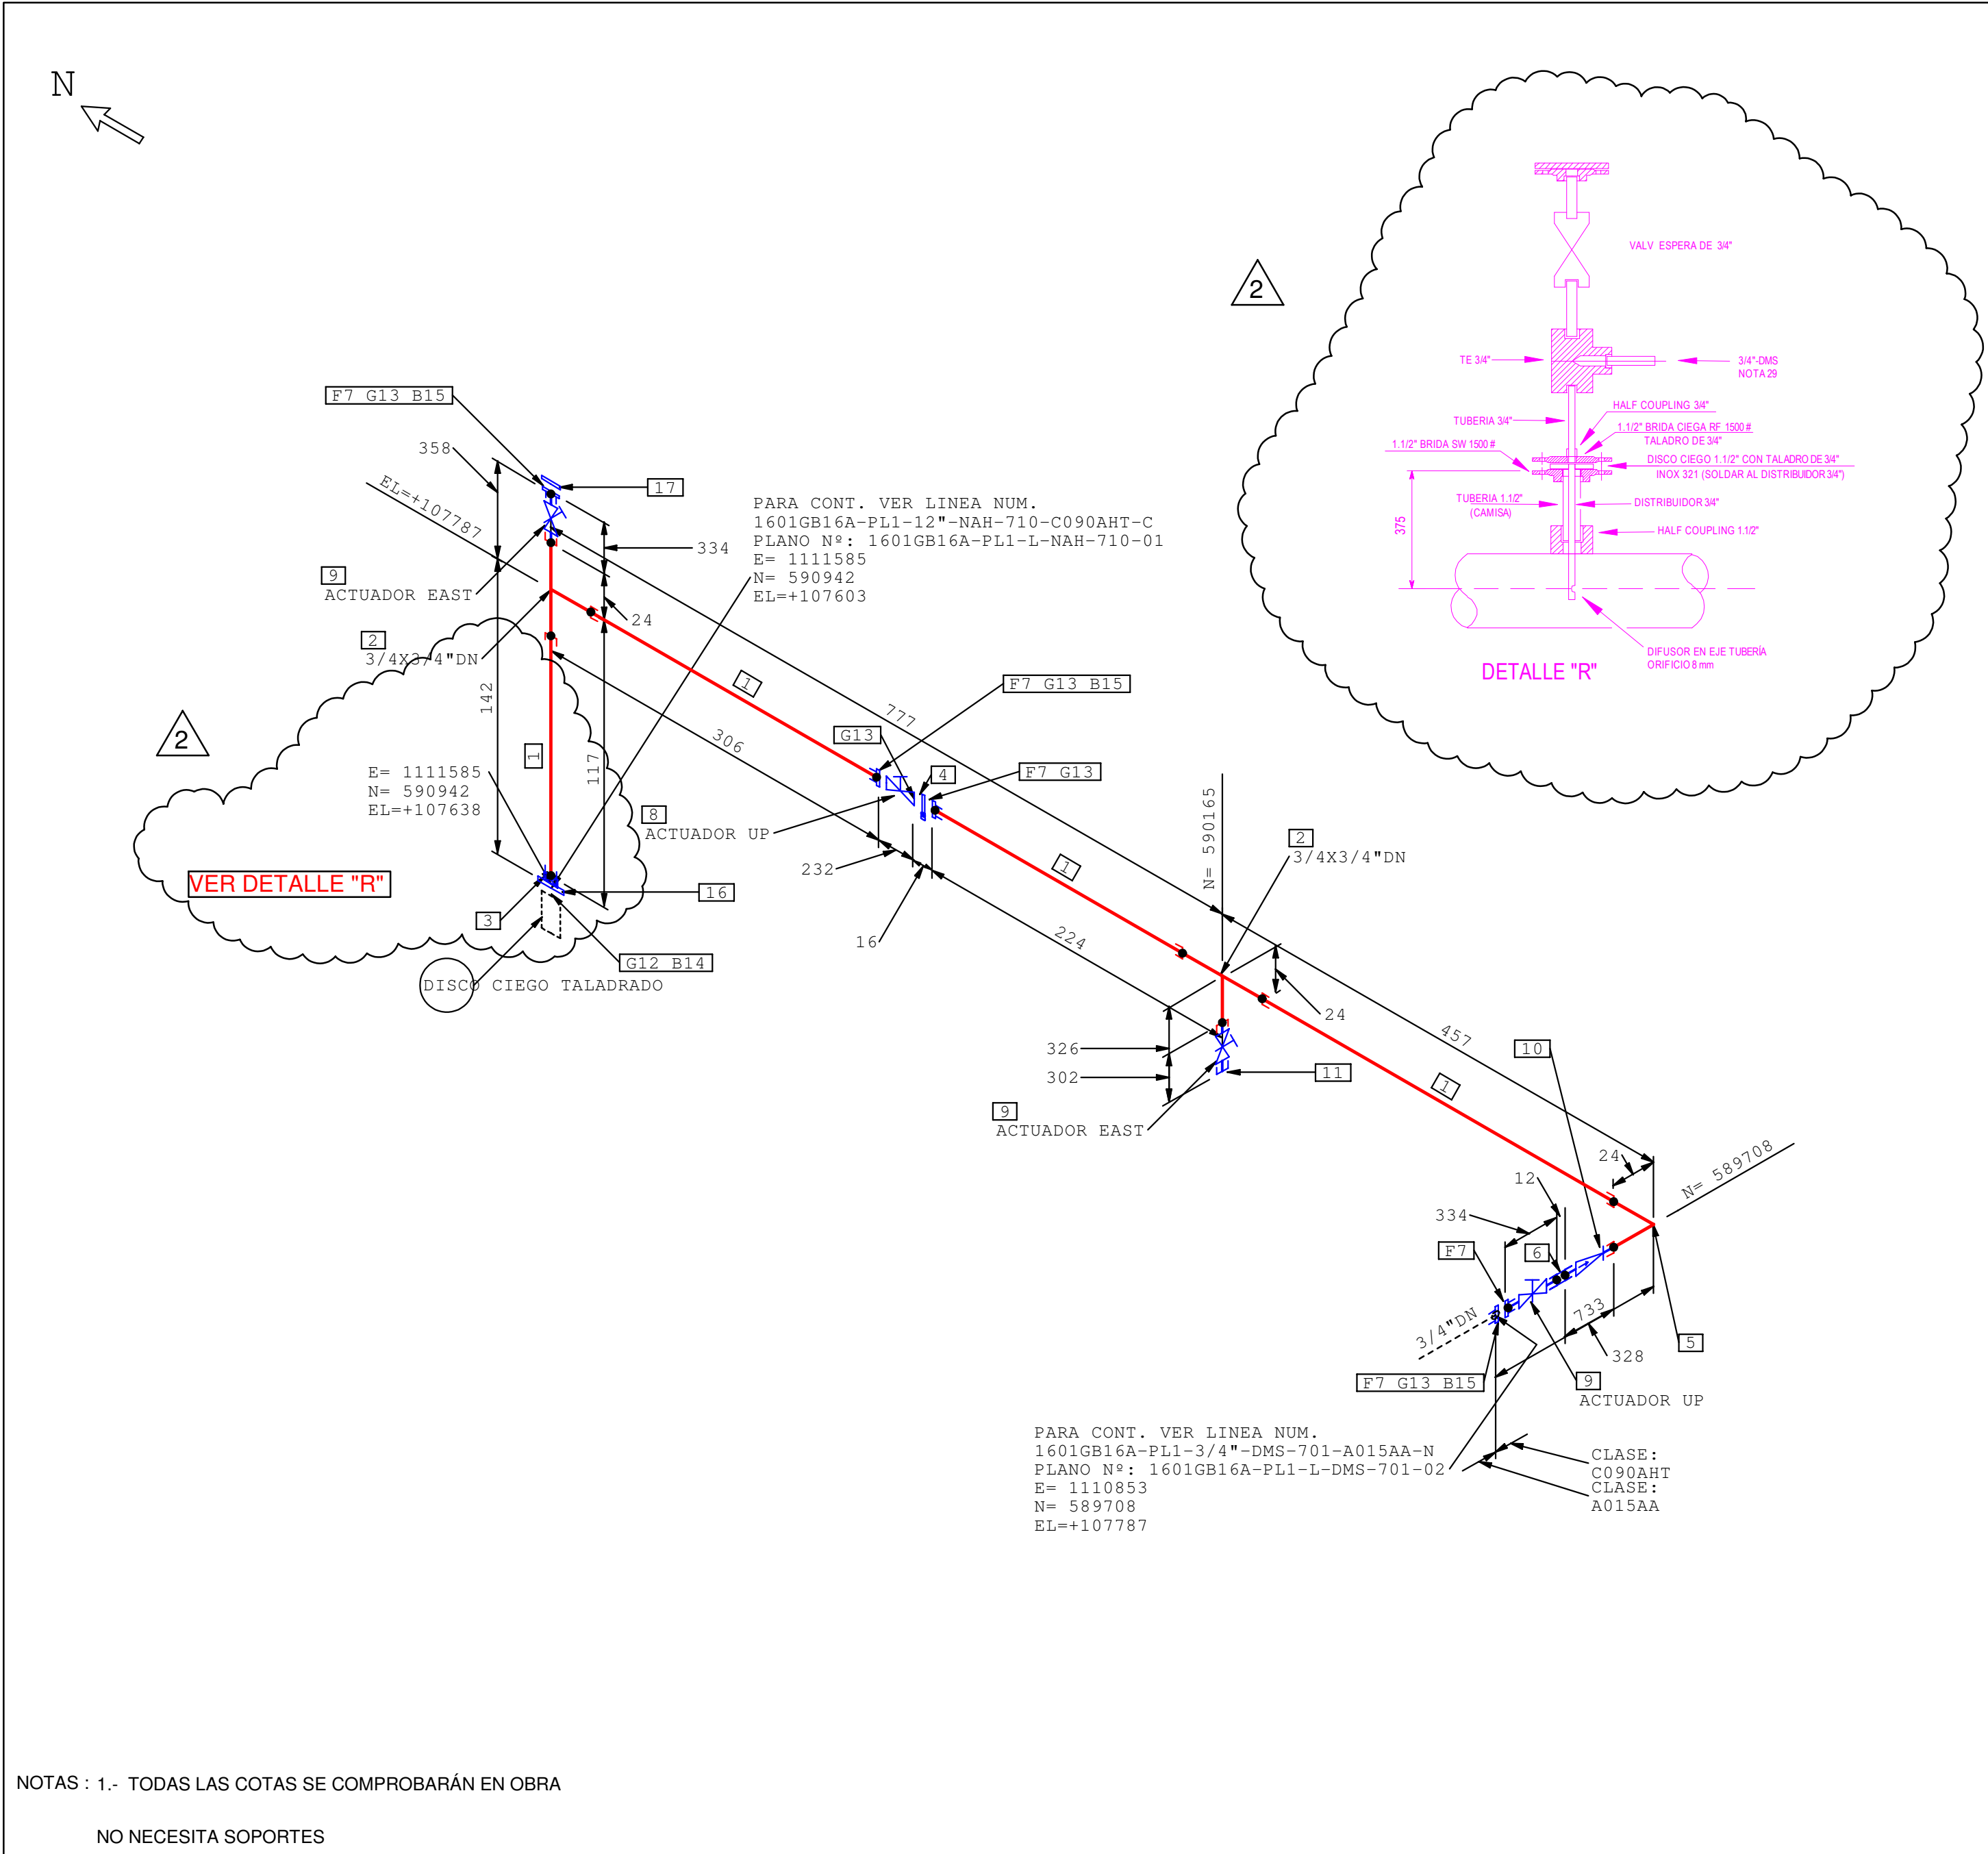

NOTAS : 1.- TODAS LAS COTAS SE COMPROBARÁN EN OBRA

NO NECESITA SOPORTES

LINEA NUM.	1601GB16A-PL1-3/4"-DMS-704-C090AHT-N	CLASE	C090AHT							
PRESIÓN OPERACIÓN kg/cm ² g	10.00	TEMPERATURA OPERACIÓN °C	40							
PRESIÓN DISEÑO kg/cm ² g	36.50	TEMPERATURA DISEÑO °C	538	2	INCLUYE INYECCION QUIMICOS	03-02-2021	FGA	RGG	FGA	PCS FAF
PRESIÓN PRUEBA kg/cm ² g	173.81	TRATAMIENTO TÉRMICO	SI	1	EMITIDO PARA CONSTRUCCIÓN	20-05-2020	TAI	NAB	JAJ	JPO REG
ESPESOR DE CALORIFUGADO		PINCHAZO N°		0	EMITIDO PARA DISEÑO	03-03-2020	TAI		JAJ	JPO
				REVISIÓN	DESCRIPCIÓN	FECHA	POR	STRESS	COMP.	APROB. V.B.

RELACIÓN DE MATERIALES

ITEM	CANT.	CÓDIGO SAP	DESCRIPCIÓN
1	1.0 M	1000937596	3/4" SCH 160 TUBERIA EXT. PLANOS A.AL. A-335 P11 ESP-1300-3 T>450°C
2	2	1000937706	3/4" TE SW 6000# A.AL. A-182 F11 ESP-1300-3 T>450°C
3	1	1000938123	3/4" HALF COUPLING SW 6000# A.AL. A-182 F11 ESP-1300-3 T>450°C
4	1	1000196324	3/4" FIGURA 8 1500# RF AA A-387 GR11 CL1 ESP-1300-3 T>450°C
5	1	1000937777	3/4" CODO 90 SW 6000# A.AL. A-182 F11 ESP-1300-3 T>450°C
6	1	1000938117	3/4" COUPLING SW 6000# A.AL. A-182 F11 ESP-1300-3 T>450°C
7	5	1000938214	3/4" SCH 160 BRIDA SW RF 1500# AA A-182 F11 ESP-1300-3 T>450°C
8	1	1000938321	3/4" VALVULA COMPUERTA FORJADA C-238
9	3	1000938311	3/4" VALVULA COMPUERTA FORJADA C-236
10	1	1000938368	3/4" VALVULA RETENCION FORJADA R-220
11	1	1000937749	3/4" CAP ROSC. 6000# A.AL. A-182 F11 ESP-1300-3 T>450°C
12	1	1001163204	1.1/2" JUNTA ESPIROM. 1500#ASME B16.5 RF 321+THC835 321
13	5	1000024376	3/4" JUNTA ESPIROM. 1500# RF 321+G AI 321
14	4	1000927018	1"x190mm ESPARRAGO+2 TUERCAS A.AL. B16/4
15	12	1000927008	3/4"x120mm ESPARRAGO+2 TUERCAS A.AL. B16/4
16	1	1000938243	1.1/2" BRIDA CIEGA RF 1500# AA A-182 F11 ESP-1300-3 T>450°C
17	1	1000938241	3/4" BRIDA CIEGA RF 1500# AA A-182 F11 ESP-1300-3 T>450°C

	PROYECTO: 1601GB16A-REVAMPING DE PLATFORMING R-98		TITULO	1601GB16A-PL1-3/4"-DMS-704-C090AHT-N-01	FORMATO	A2
	UNIDAD: SR-01-A01-PL1 UNIDAD DE PLATFORMING					
	PLANTA: SR01 PLANTA DE AROMATICOS					
	LOCALIZACIÓN: REFINERIA DE GIBRALTAR. SAN ROQUE					
	INGENIERIA Y SISTEMAS, S.A.					
P&ID NUMERO			PLANO NUMERO			REV.
1601GB16A-302-X-9			1601GB16A-PL1-L-DMS-704-01			2