


ACTUALIZACIÓN: 09/02/2021 10:59:42

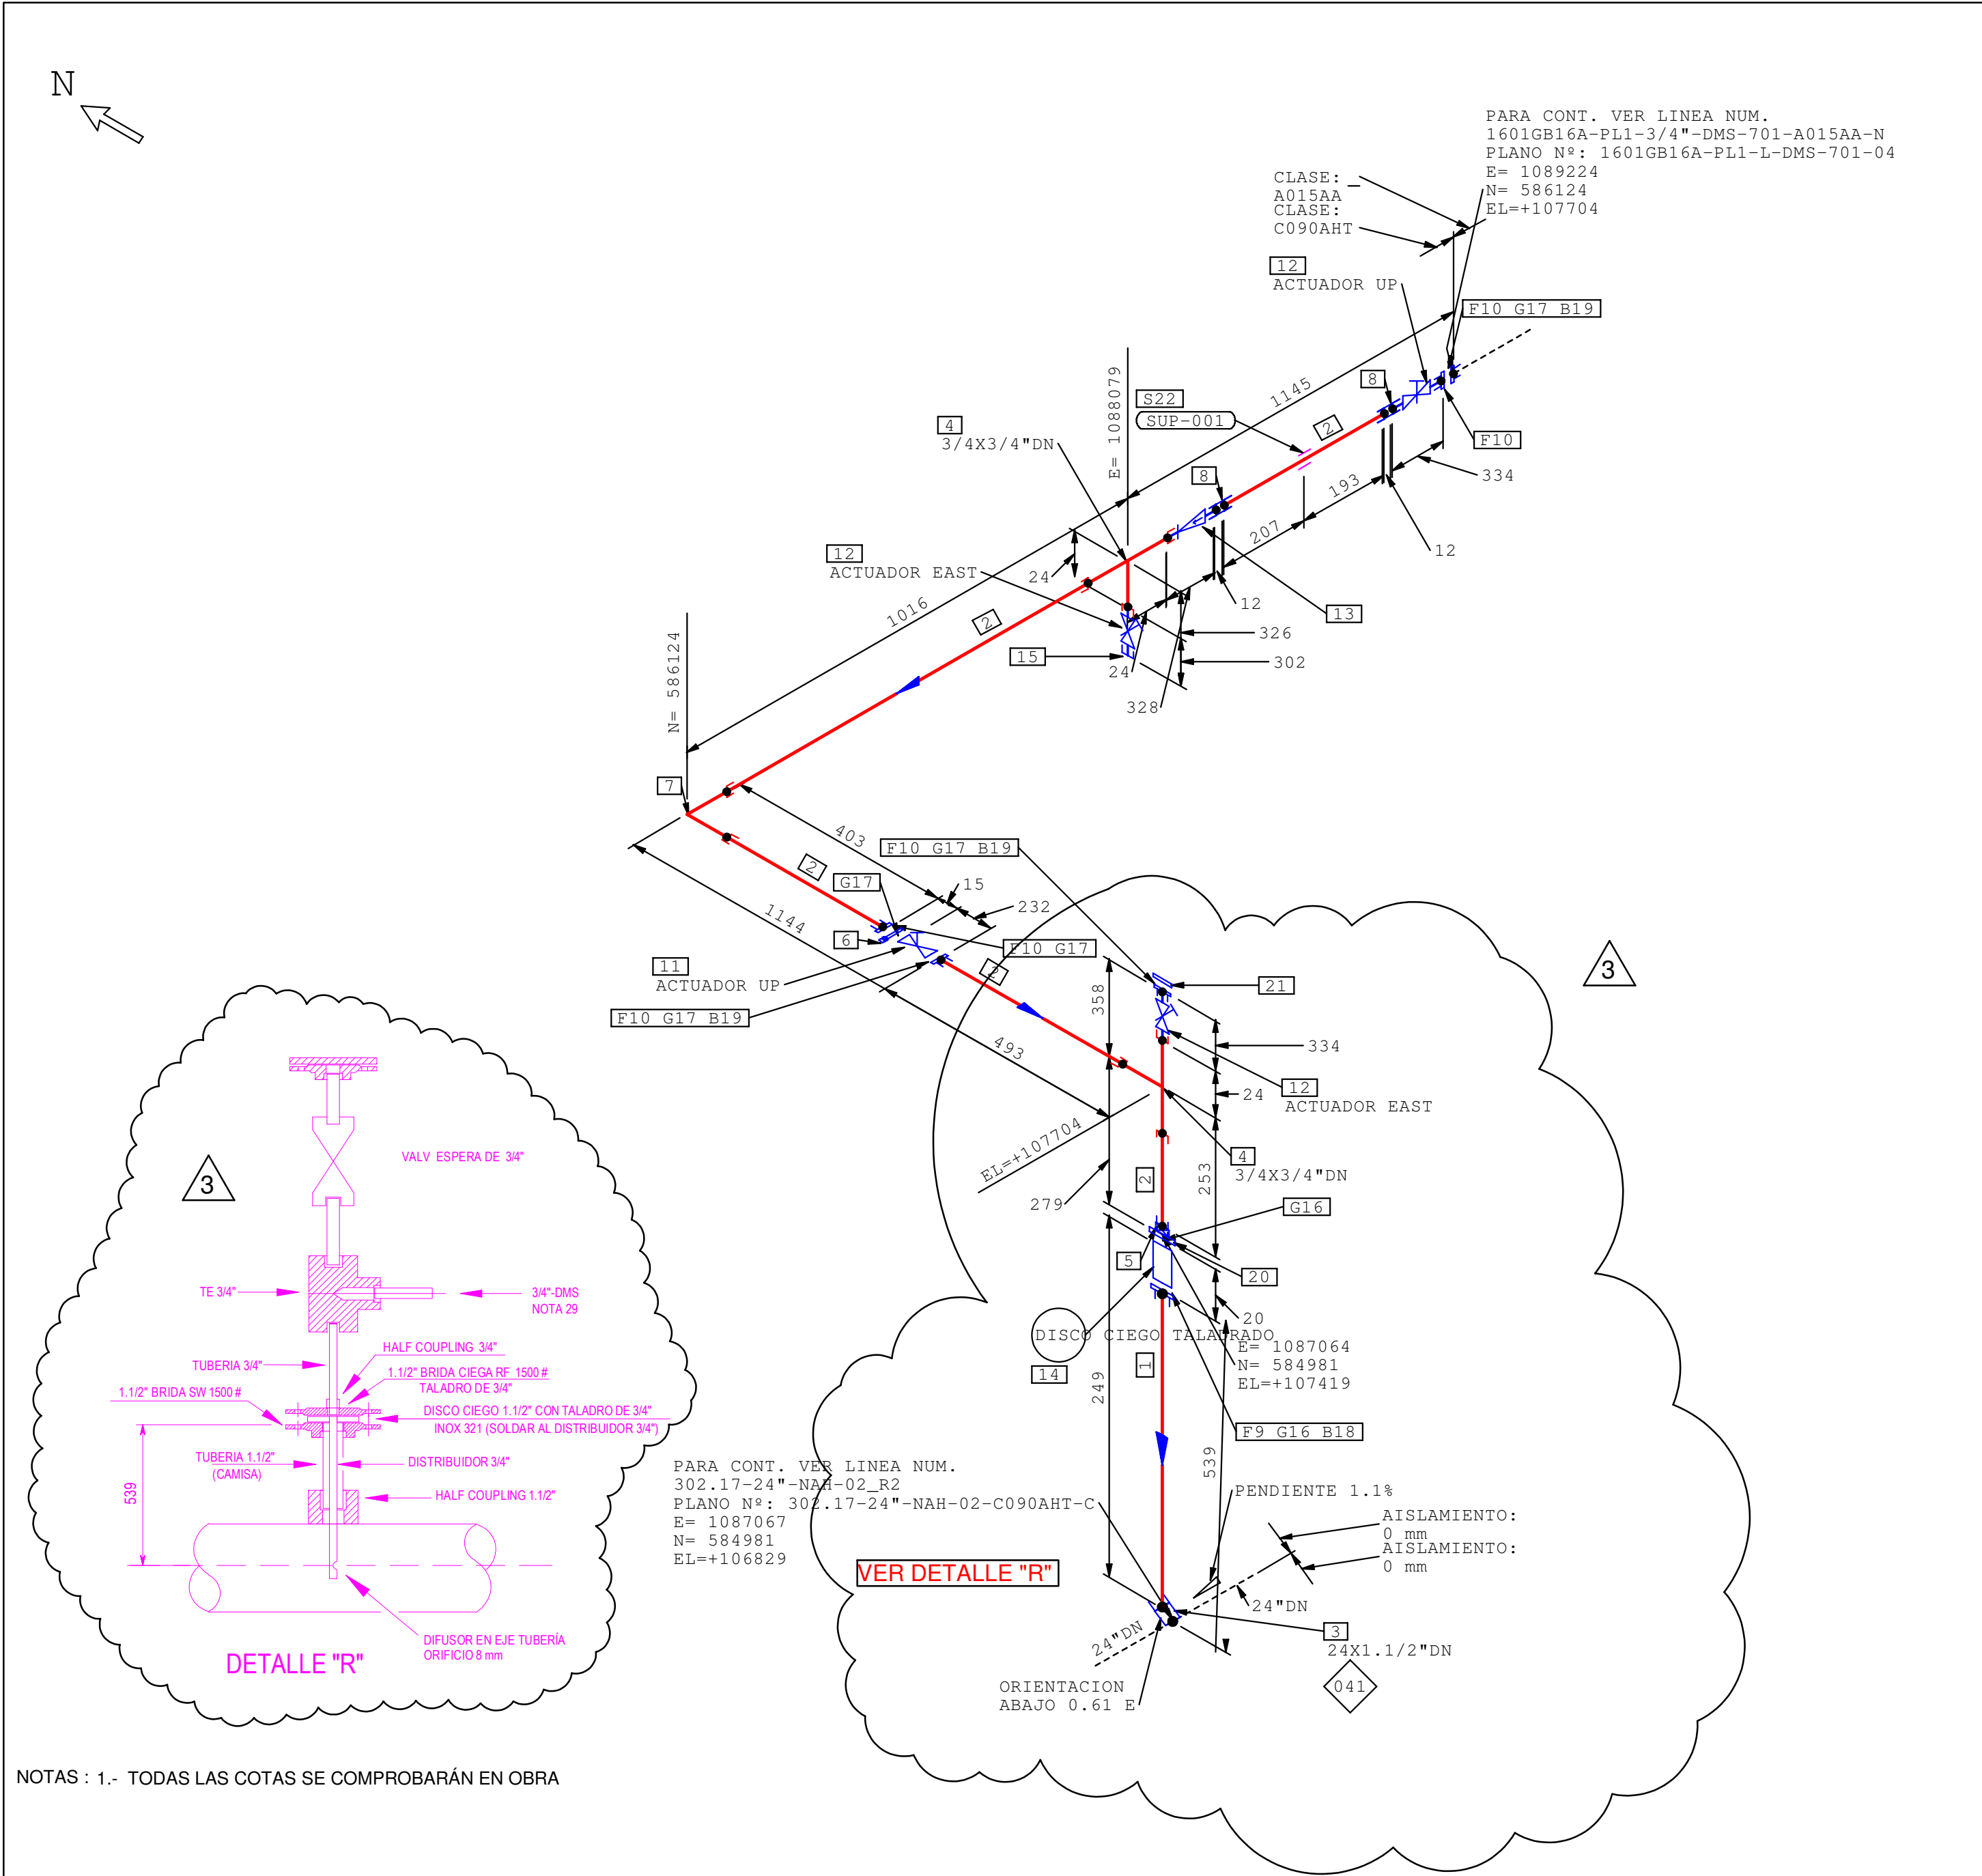

NOTAS : 1.- TODAS LAS COTAS SE COMPROBARÁN EN OBRA

LINEA NUM.	1601GB16A-PL1-3/4"-DMS-703-C090AHT-N	CLASE	C090AHT							
PRESIÓN OPERACIÓN kg/cm ² g	10.00	TEMPERATURA OPERACIÓN °C	40							
PRESIÓN DISEÑO kg/cm ² g	31.50	TEMPERATURA DISEÑO °C	538	3	INCLUYE INYECCION QUIMICOS	03-02-2021	FGA	FAF	FGA	PCS
PRESIÓN PRUEBA kg/cm ² g	150.00	TRATAMIENTO TÉRMICO	SI	2	REVISADO LO REVISADO	22-06-2020	TAI		JAJ	JPO
ESPESOR DE CALORIFUGADO		PINCHAZO N°	041	1	EMITIDO PARA CONSTRUCCIÓN	20-05-2020	TAI	NAB	JAJ	JPO
				0	EMITIDO PARA DISEÑO	03-03-2020	TAI		JAJ	JPO
				REVISIÓN	DESCRIPCIÓN	FECHA	POR	STRESS	COMP.	APROB.
										V.B.

RELACIÓN DE MATERIALES

ITEM	CANT.	CÓDIGO SAP	DESCRIPCIÓN
1	0.2 M	1000937601	1.1/2" SCH 160 TUBERIA EXT. PLANOS A.AL. A-335 P11 ESP-1300-3 T>450°C
2	2.4 M	1000937596	3/4" SCH 160 TUBERIA EXT. PLANOS A.AL. A-335 P11 ESP-1300-3 T>450°C
3	1	1000938125	1.1/2" HALF COUPLING SW 6000# A.AL. A-182 F11 ESP-1300-3 T>450°C
4	2	1000937706	3/4" TE SW 6000# A.AL. A-182 F11 ESP-1300-3 T>450°C
5	1	1000938123	3/4" HALF COUPLING SW 6000# A.AL. A-182 F11 ESP-1300-3 T>450°C
6	1	1000196324	3/4" FIGURA 8 1500# RF AA A-387 GR11 CL1 ESP-1300-3 T>450°C
7	1	1000937777	3/4" CODO 90 SW 6000# A.AL. A-182 F11 ESP-1300-3 T>450°C
8	2	1000938117	3/4" COUPLING SW 6000# A.AL. A-182 F11 ESP-1300-3 T>450°C
9	1	1000938217	1.1/2" SCH 160 BRIDA SW RF 1500# AA A-182 F11 ESP-1300-3 T>450°C
10	5	1000938214	3/4" SCH 160 BRIDA SW RF 1500# AA A-182 F11 ESP-1300-3 T>450°C
11	1	1000938321	3/4" VALVULA COMPUERTA FORJADA C-238
12	3	1000938311	3/4" VALVULA COMPUERTA FORJADA C-236
13	1	1000938368	3/4" VALVULA RETENCION FORJADA R-220
14	1	-	DISCO CIEGO TALADRADO
15	1	1000937749	3/4" CAP ROSC. 6000# A.AL. A-182 F11 ESP-1300-3 T>450°C
16	2	1001163204	1.1/2" JUNTA ESPIROM. 1500#ASME B16.5 RF 321+THC835 321
17	5	1000024376	3/4" JUNTA ESPIROM. 1500# RF 321+G AI 321
18	4	1000927018	1"x190mm ESPARRAGO+2 TUERCAS A.AL. B16/4
19	12	1000927008	3/4"x120mm ESPARRAGO+2 TUERCAS A.AL. B16/4
20	1	1000938243	1.1/2" BRIDA CIEGA RF 1500# AA A-182 F11 ESP-1300-3 T>450°C
21	1	1000938241	3/4" BRIDA CIEGA RF 1500# AA A-182 F11 ESP-1300-3 T>450°C
SOPORTES			
22	1	SUP-001	STD-PS-050 (PSL)

	PROYECTO:	1601GB16A-REVAMPING DE PLATFORMING R-98	
	UNIDAD:	SR-01-A01-PL1 UNIDAD DE PLATFORMING	
	PLANTA:	SR01 PLANTA DE AROMATICOS	
	LOCALIZACIÓN:	REFINERIA DE GIBRALTAR. SAN ROQUE	
TÍTULO		1601GB16A-PL1-3/4"-DMS-703-C090AHT-N-01	FORMATO
P&ID NUMERO		1601GB16A-302-X-9	A2
PLANO NUMERO		1601GB16A-PL1-L-DMS-703-01	REV.
			3